ЛИМЦ.60148.12.000.001

Перв. примен.	ЛИМЦ.60148.00.000.000
Справ. №	
Подп. и дата	
Инв. № дубл.	
Взам. инв. №	
Подп. и дата	
Инв. № подл.	

Ra 12,5 (√)

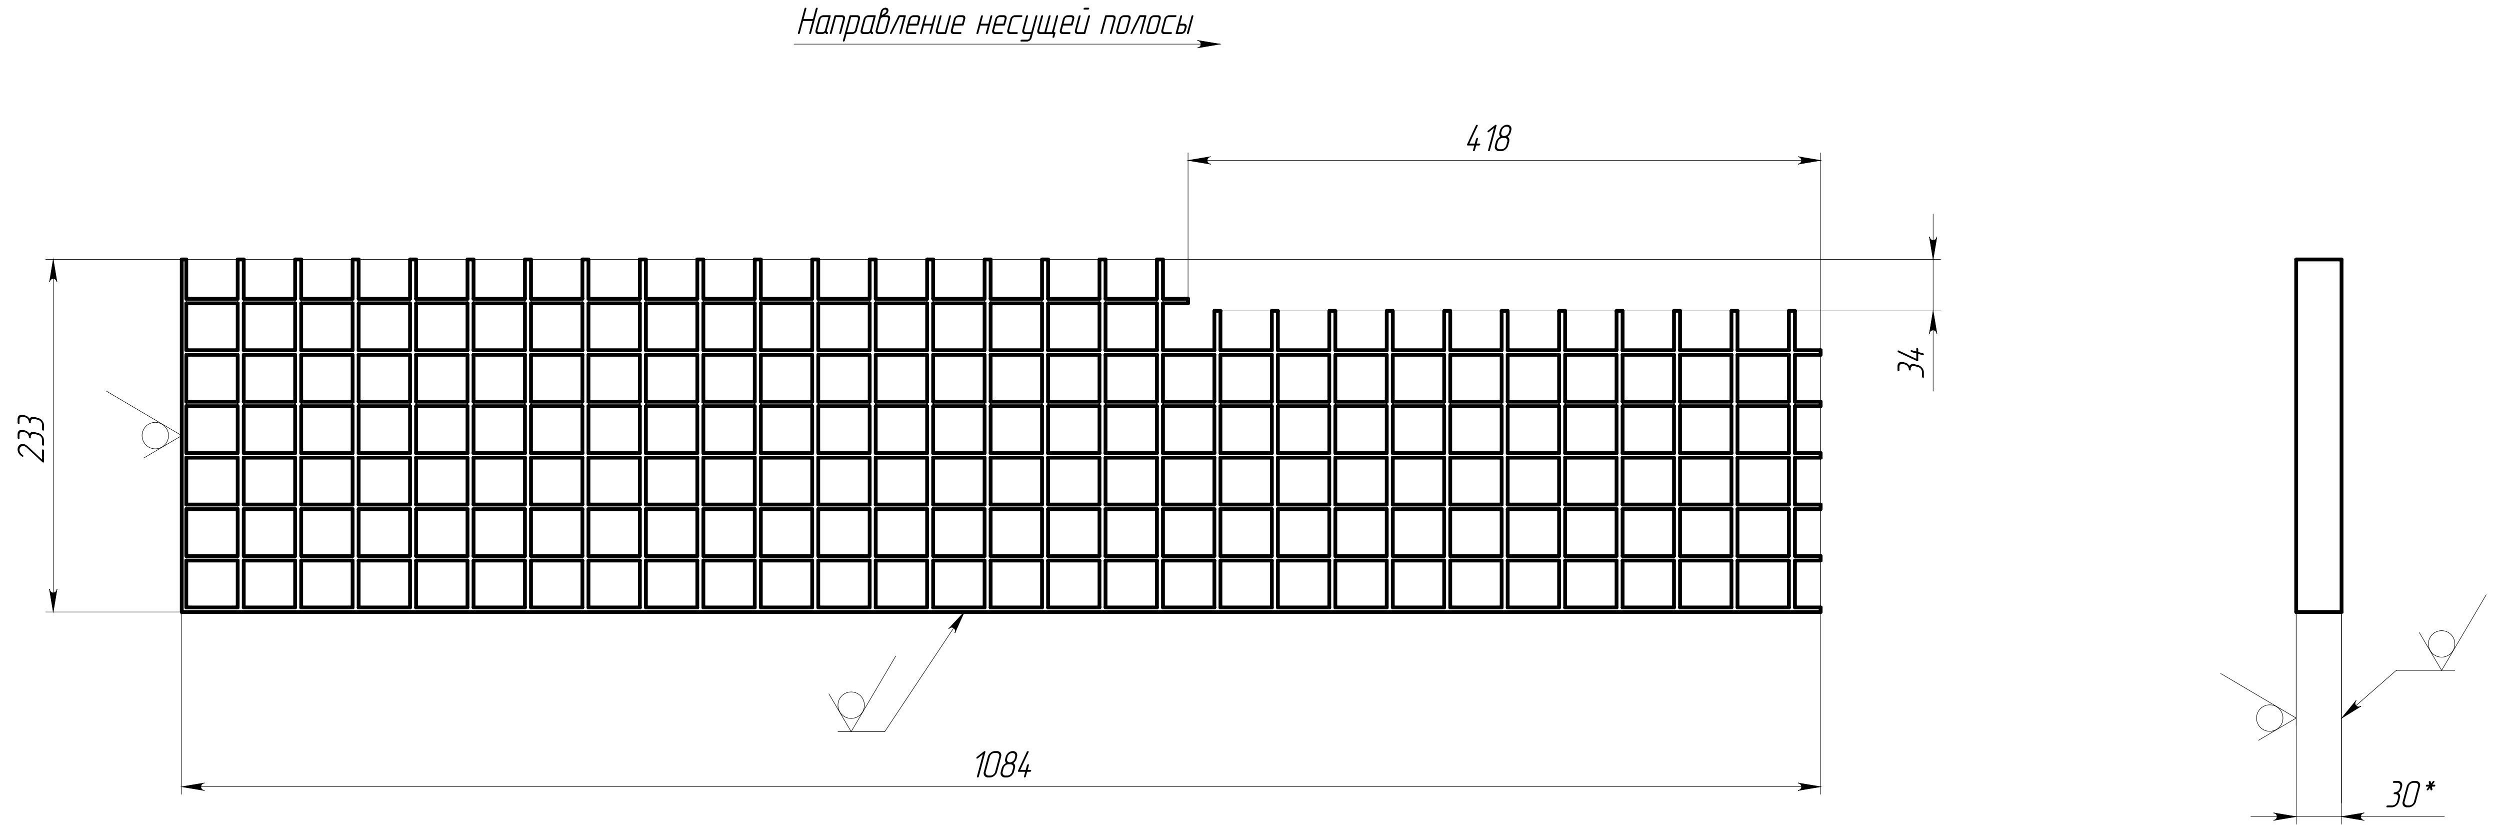

Направление несущей полосы
418
34
233
1084
30*

1. *ǔǫǅǶǯǺ ǯǵǐ̀ ǻǹǺǫǭǸǴ.
2. Общие допуски по ГОСТ 30893.1: ±IT14/2.
3. ǖǫǺǴǅǺǸǭǫǼǨ ǸǫǸǅǷǫǟǯǷǅǯ ǟǯǺǼǯǰǫ.

Изм.	Лист	№ докум.	Подп.	Дата	ЛИМЦ.60148.12.000.001
Разраб.		Быков		28.10.25	Настил
Пров.		Лаптев			
Т. контр.					
Н. контр.					
Утв.		Соломатин			Настил SP 34x38/30x3, S4, Zn, тип A

Лит.	Масса	Масштаб
	6.95	1:5
Лист	Листов 1	

АО "БТ"

Копировал

Формат А3