ЛИМЦ.60148.12.000.001-01

Перв. примен.
ЛИМЦ.60148.00.000.000
Справ. №

√ Ra 12,5 (√)

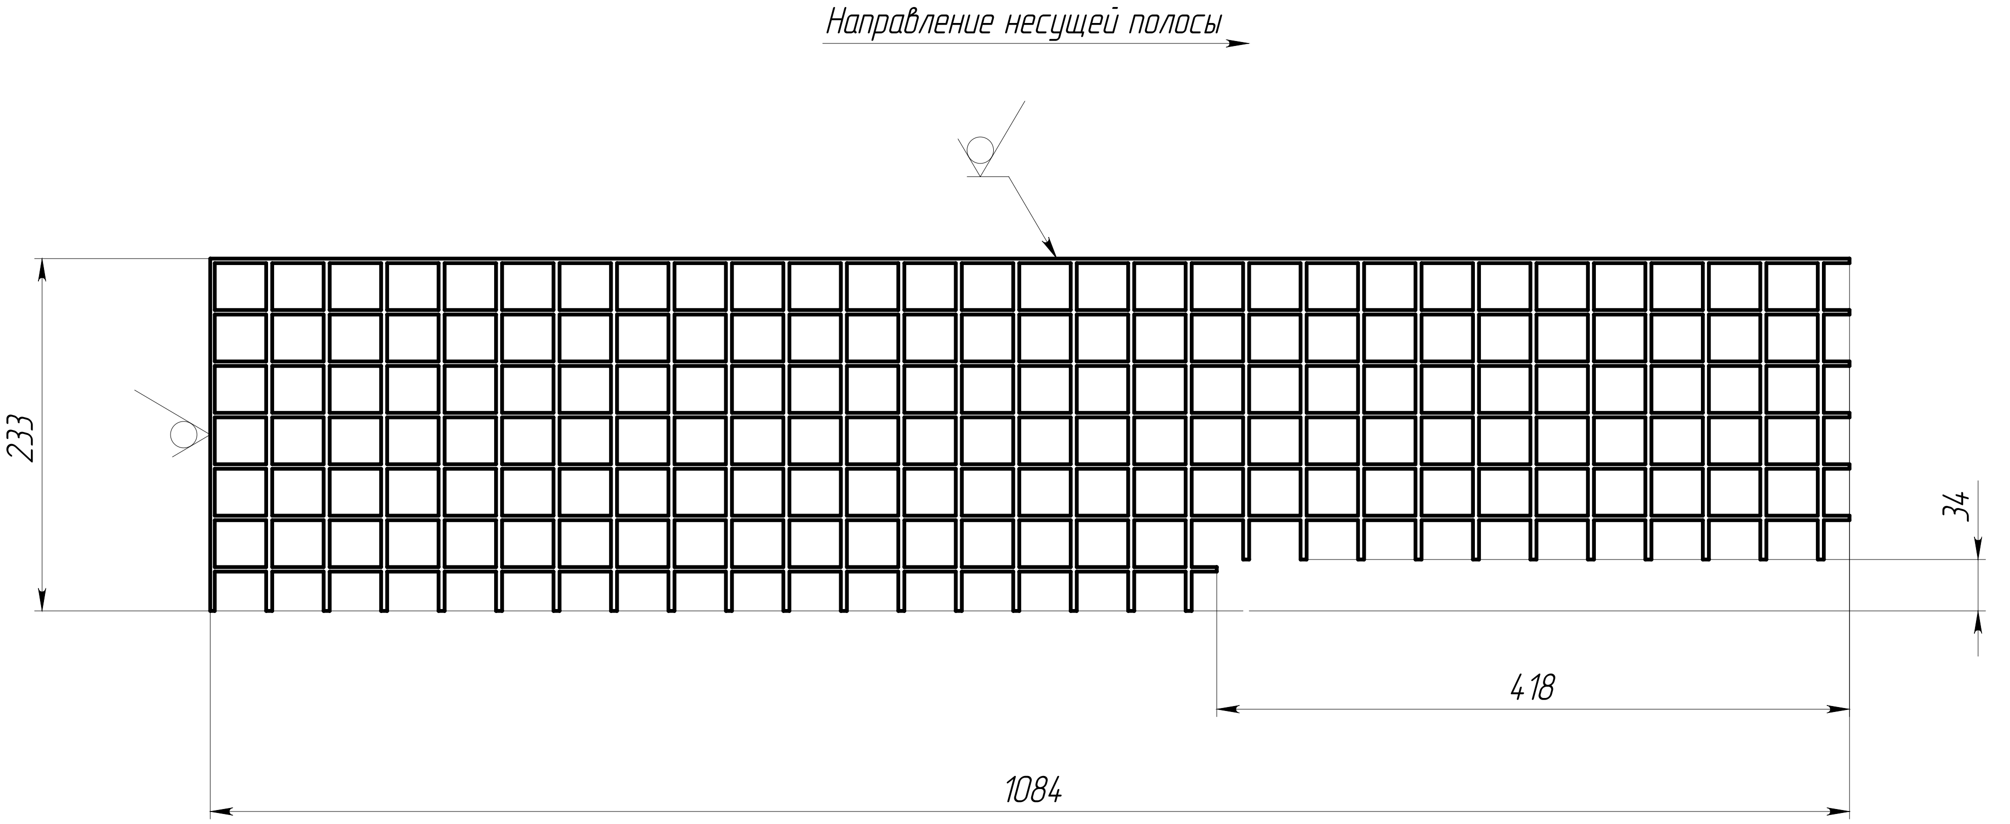

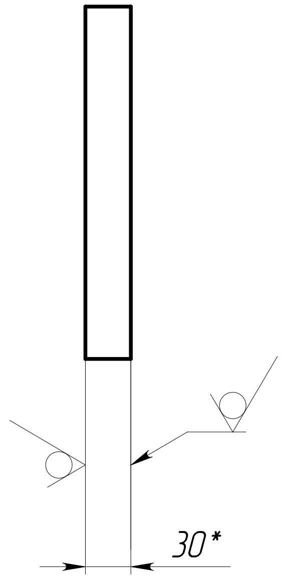

1. *ŭϘDzHȝÁ ȝǵĩ ǻǹÅϘϘ̄ǸǴ.
2. Общие допуски по ГОСТ 30893.1: ±IT14/2.
3. ŭϘÅǴDzÅǸϘϘǼÊ ǸϘǸDzϷϘäȝϷDzȝ äȝÅǼȝĵϘ.

Подп. и дата
Инв. № дубл.
Взам. инв. №
Подп. и дата
Инв. № подл.

Изм. | Лист | № докум. | Подп. | Дата
Разраб. Быков 28.10.25
Пров. Лаптев
Т. контр.
Н. контр.
Утв. Соломатин

ЛИМЦ.60148.12.000.001-01

Настил

Лит. | Масса | Масштаб
6.95 | 1:5
Лист | Листов 1

Настил SP 34x38/30x3, S4, Zn, тип А

АО "БТ"

Копировал
Формат А3