ЛИМЦ.60148.12.000.003

Перв. примен.	ЛИМЦ.60148.00.000.000
Справ. №	
Подп. и дата	
Инв. № дубл.	
Взам. инв. №	
Подп. и дата	
Инв. № подл.	

Ra 12,5 (√)

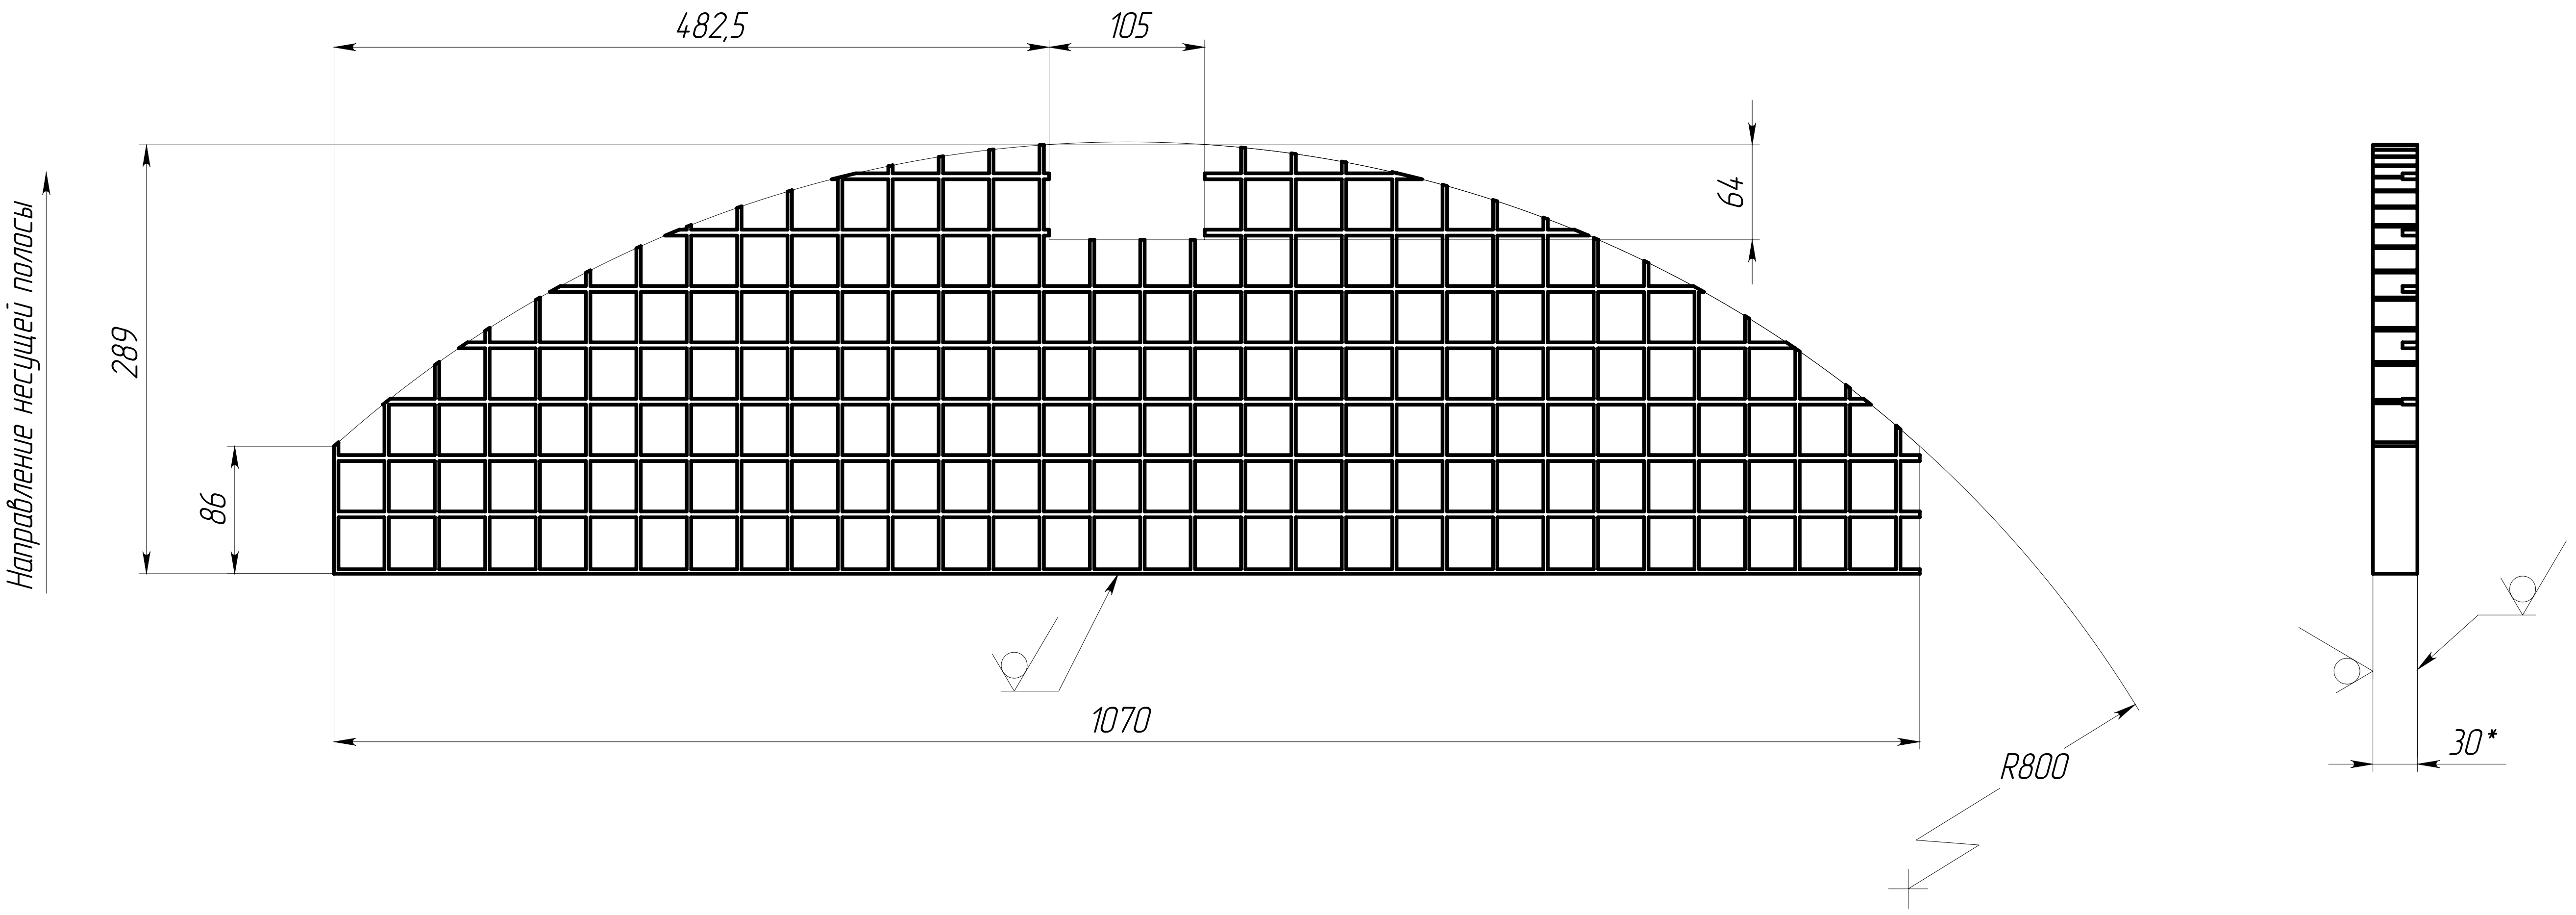

482,5
105
64
289
86
1070
R800
30*
Направление несущей полосы

1. *ŭǫǲǶǯÁ ǯǵì áǹÅǫǫÑǴ.
2. Общие допуски по ГОСТ 30893.1: ±IT14/2.
3. ŭǫÅǴǲÅÑǫǫÆÊ ÑǫÑǲǷǫäǯǷǲǯ äǯÅÆǯǰǫ.

ЛИМЦ.60148.12.000.003

Изм.	Лист	№ докум.	Подп.	Дата
Разраб.		Быков		28.10.25
Пров.		Лаптев		
Т. контр.				
Н. контр.				
Утв.		Соломатин		

Настил

Лит.	Масса	Масштаб
	7.20	1:5

Лист — Листов 1

Настил SP 34x38/30x3, S4, Zn, тип А

АО "БТ"

Копировал

Формат А3