Перв. примен.
ЛИМЦ.60148.12.001.000
Справ. №
Подп. и дата
Инв. № дубл.
Взам. инв. №
Подп. и дата
Инв. № подл.

ЛИМЦ.60148.12.001.001

√ Ra 12,5 (√)

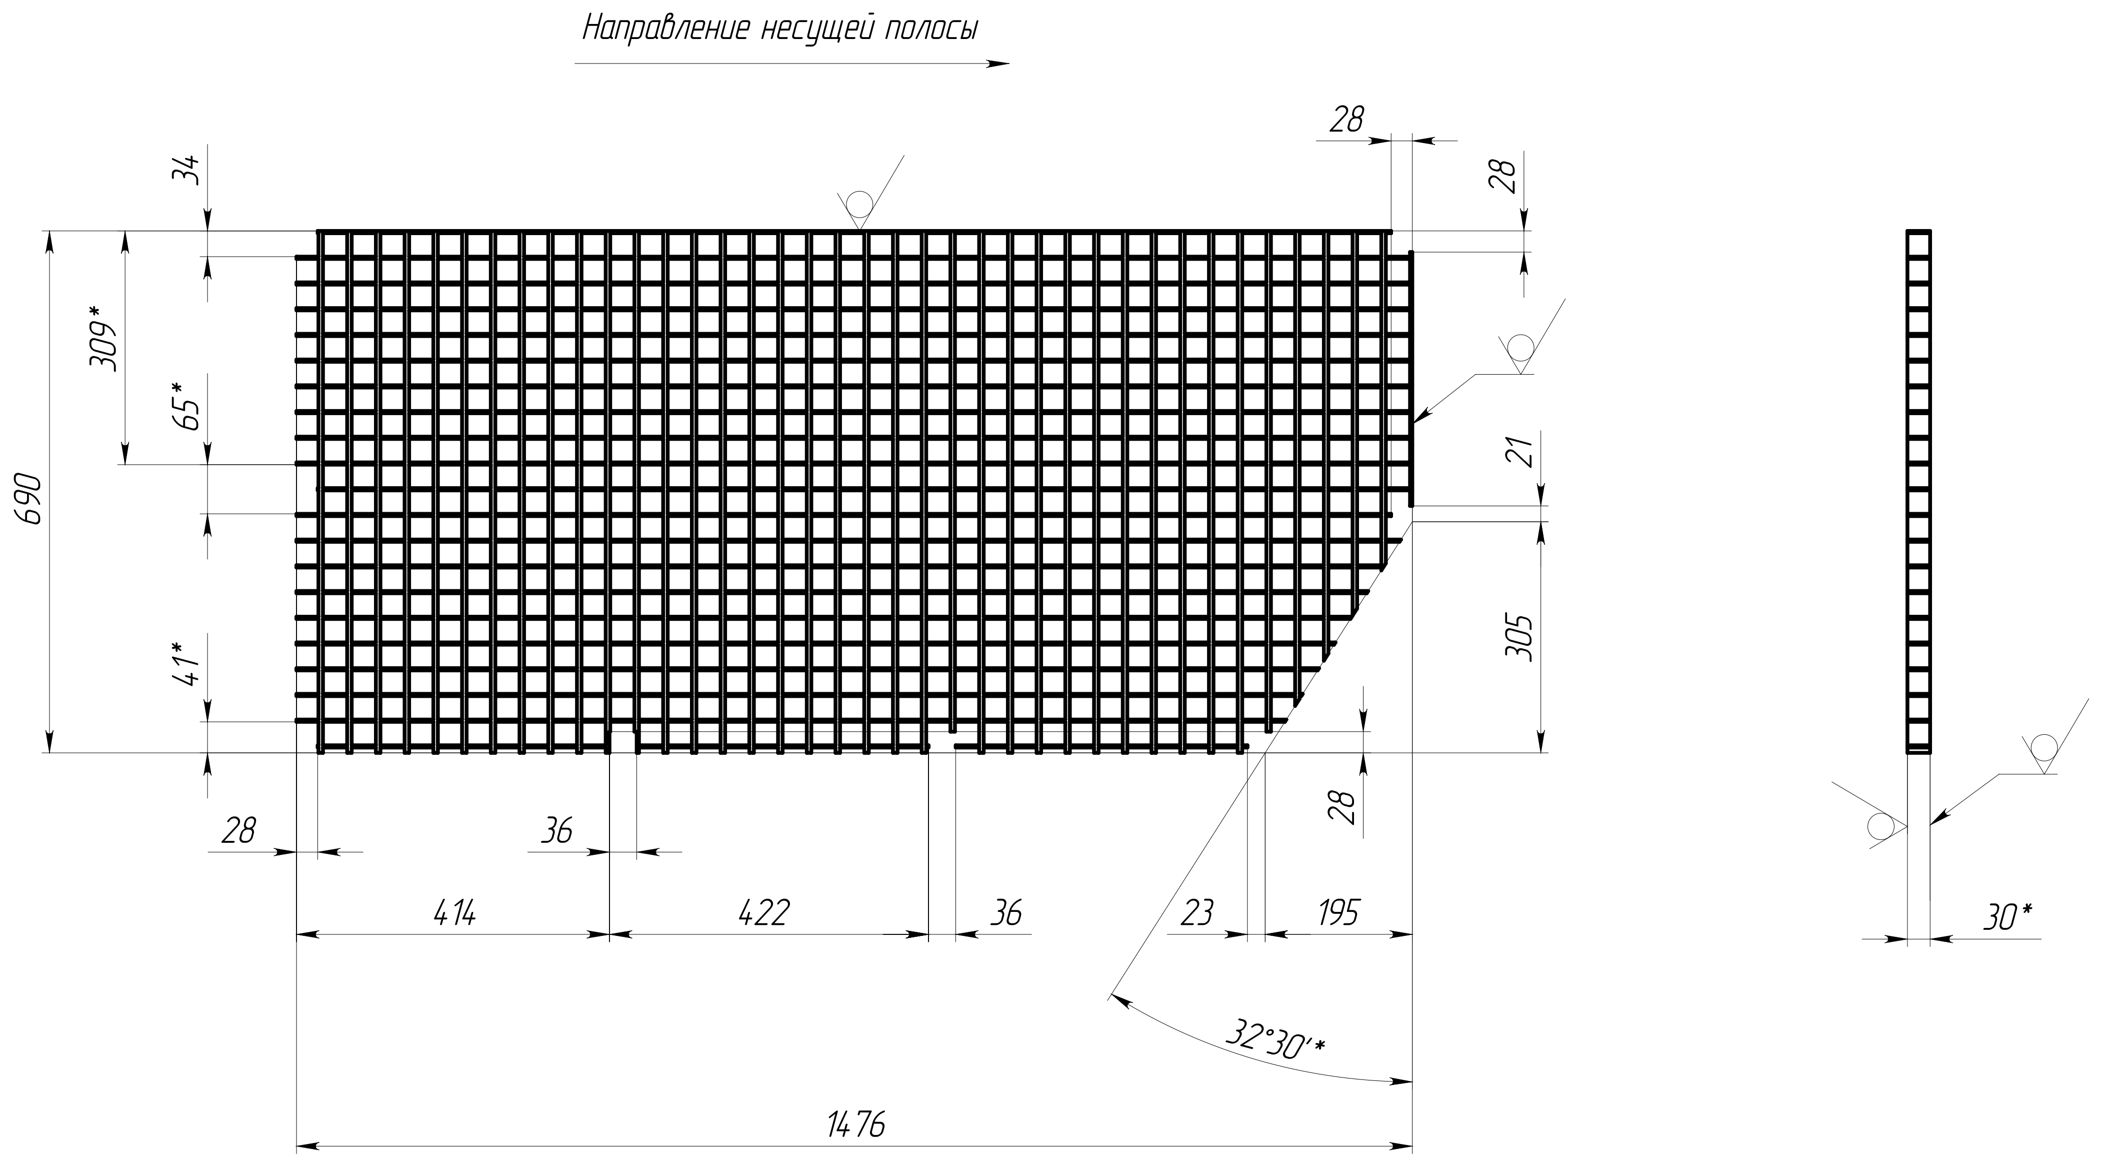

1. *ŭọǅǶʒÅȅ ǯǵȉ ǻǹǺọọŌǸǴ.
2. Общие допуски по ГОСТ 30893.1: ±IT14/2.
3. ȫọǺǴǆǺǸọọǼȆ ǸọǸǆƿọȁʒƿǆʒ ȁʒǺǼʒǰọ.

Изм.	Лист	№ докум.	Подп.	Дата	ЛИМЦ.60148.12.001.001
Разраб.		Быков		28.10.25	Настил
Пров.		Лаптев			
Т. контр.					
Н. контр.					Настил SP 34x38/30x3, S4, Zn, тип A
Утв.		Соломатин			

Лит.	Масса	Масштаб
	53.92	1:10
Лист	Листов 1	
АО "БТ"		

Копировал

Формат A3