
ЛИМЦ.6014.8.13.000.000СБ


Ж (1 : 5)
2 места

И (1 : 5)
2 места

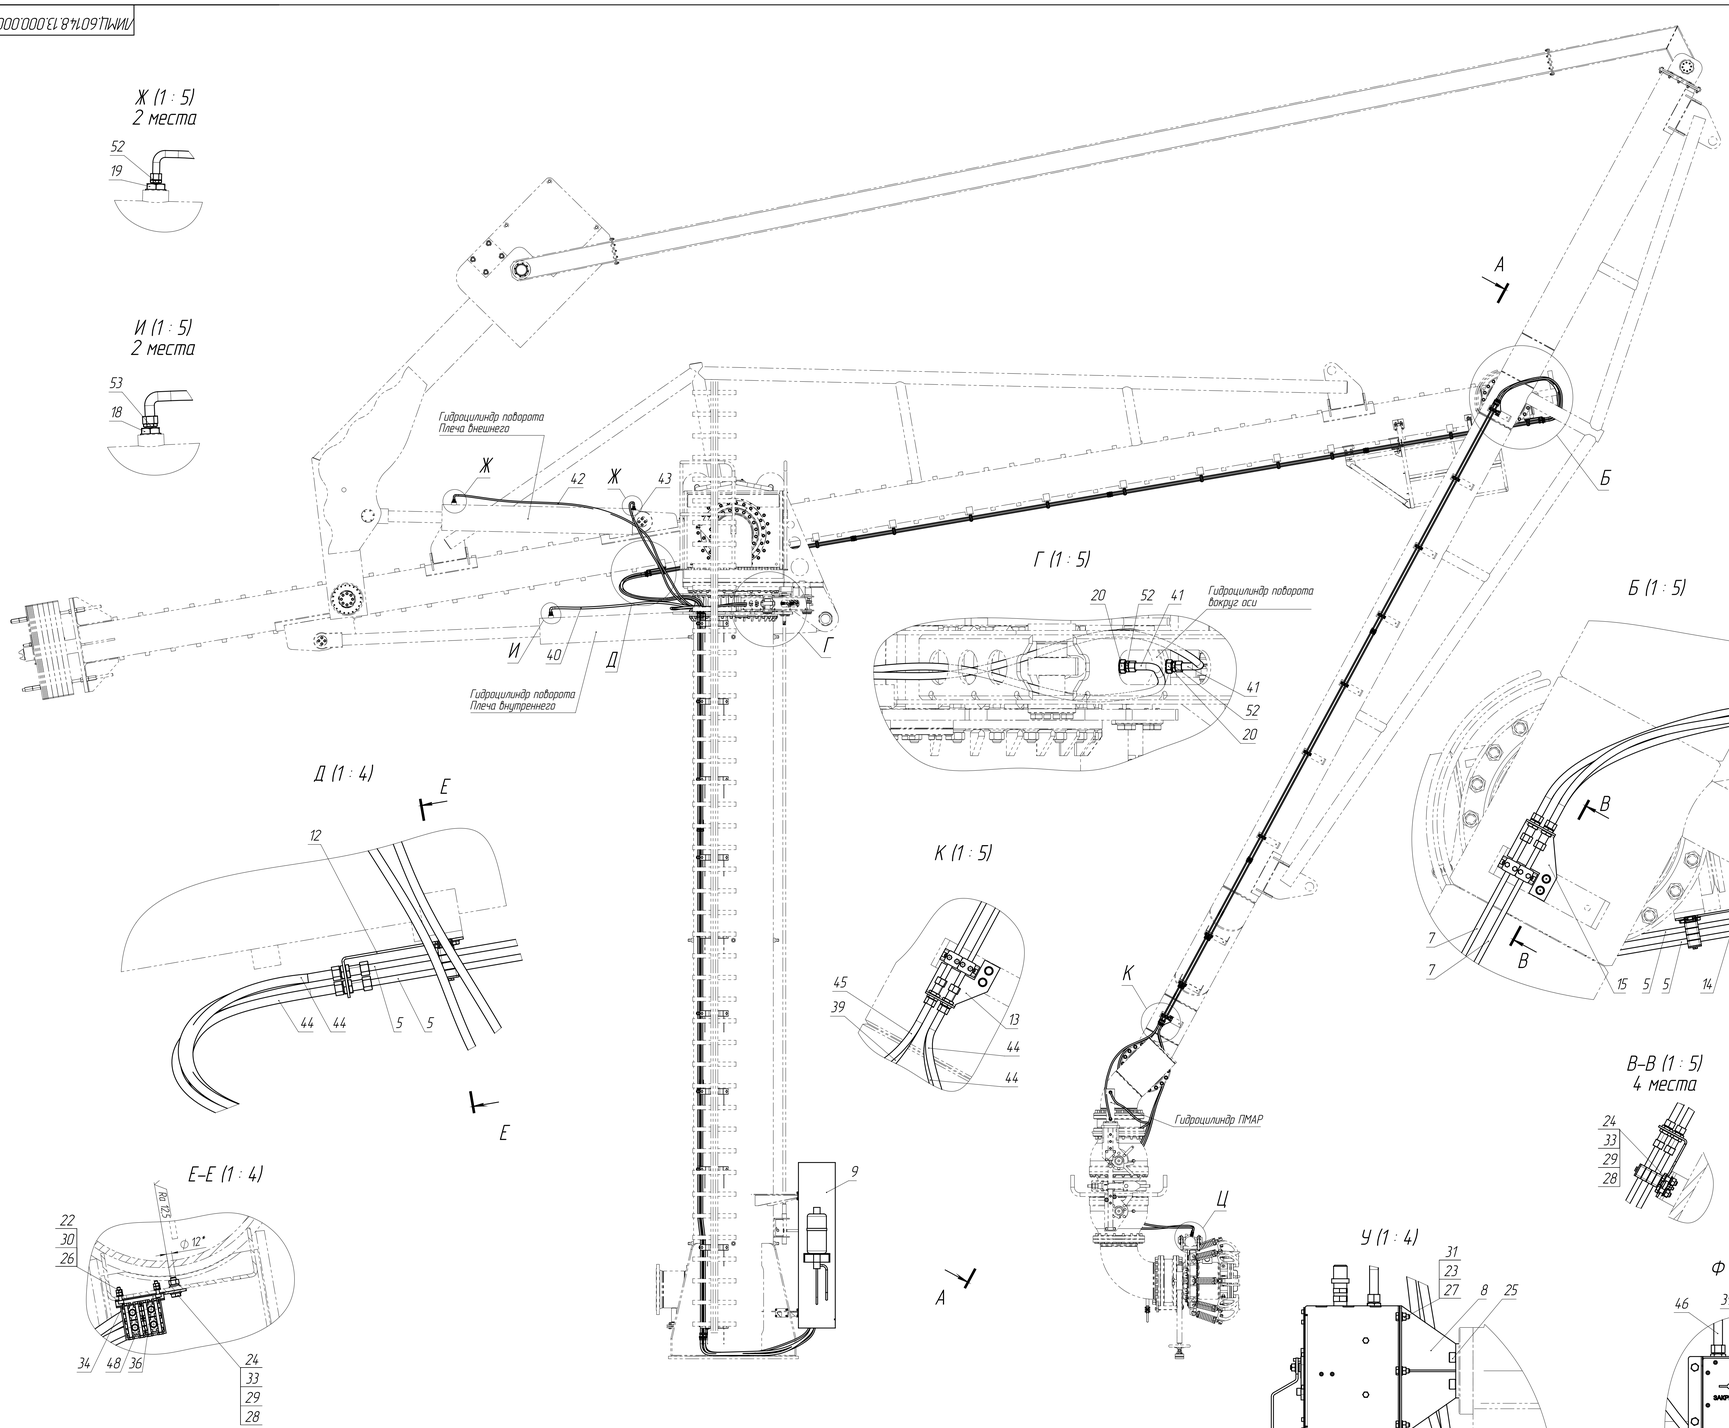


Г (1 : 5)


Б (1 : 5)

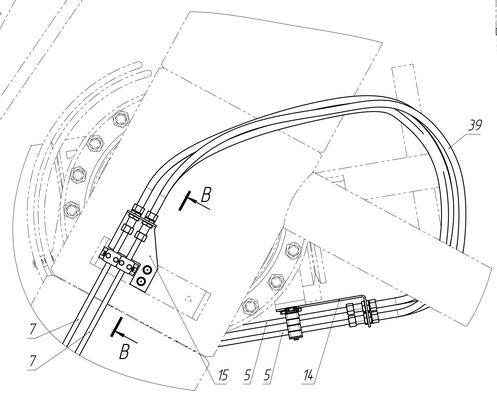



А–А

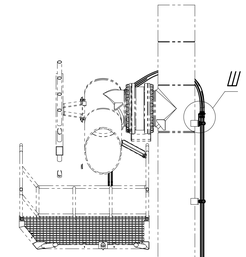

Ш (1 : 4)

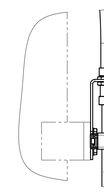

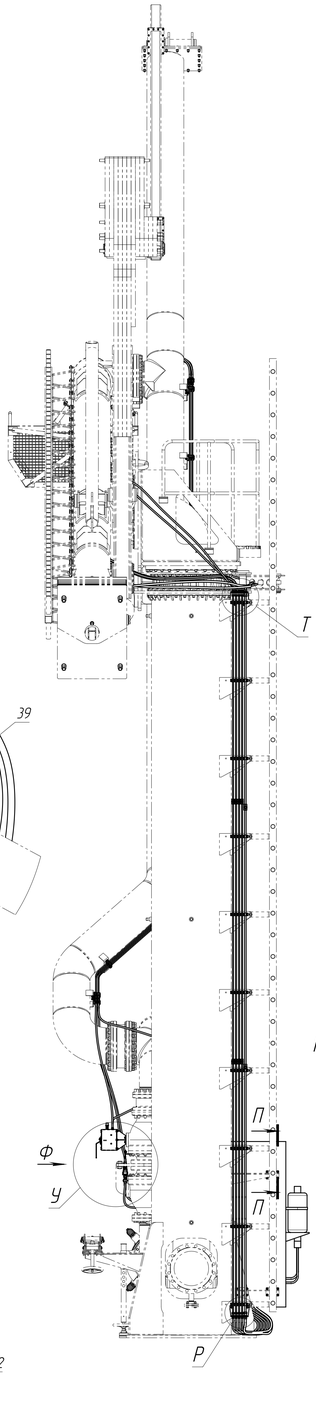

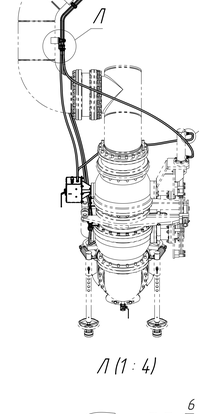


Д (1 : 4)

К (1 : 5)


А

В–В (1 : 5)
4 места

П–П (1 : 4)

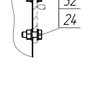


Л (1 : 4)

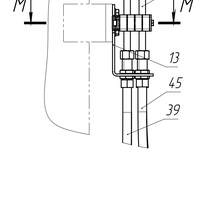


Н (1 : 5)
2 места




Е–Е (1 : 4)

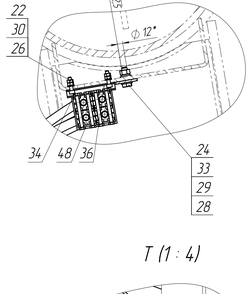


У (1 : 4)

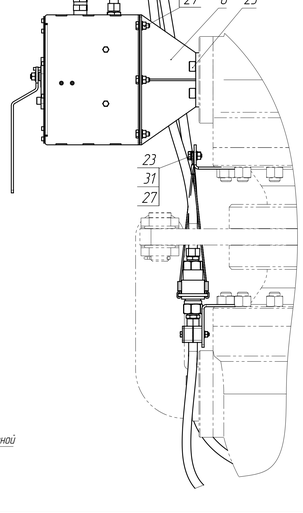


Ф (1 : 4)

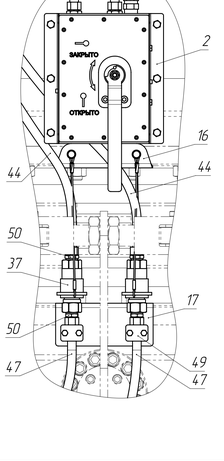


Т (1 : 4)

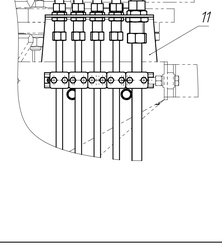


Р (1 : 4)

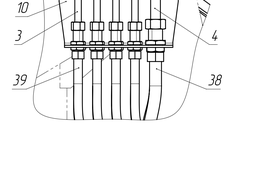


С–С (1 : 4)
10 мест

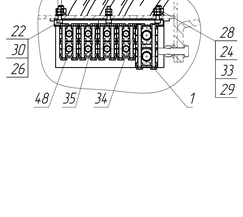

Ц (1 : 5)

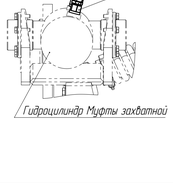

М–М (1 : 4)

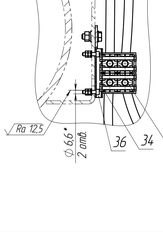

1. *Размеры для исполнения, остальные для справок.
2. Отверстия под крепеж Кронштейнов поз. 10–17 и под Планки поз. 35 и 36 выполнить по месту.
3. Подключения РВД к гидроцилиндрам и шкафу гидравлическому выполнить согласно схемы гидравлической.
4. Общие допуски по ГОСТ 30893.1 H14, h14, ±IT14/2.
5. Общие допуски формы и расположения – ГОСТ 30893.2 – K.
6. Маркировать обозначение чертежа.

					ЛИМЦ.6014.8.13.000.000СБ		
Изм.	Лист	№ докум.	Подп.	Дата	Монтаж гидрооборудования на стенде	Лит.	Масса	Масштаб
Разраб.		Нагуманов Н.Д.		12.03.26			-	1:25
Пров.		Макаров Е.В.		12.03.26				
Т. контр.		Волков И.А.		12.03.26	Сборочный чертеж	Лист	Листов 1
Н. контр.		Вяхина А.Н.		12.03.26		АО "БТ"	
Утв.		Сыкорей М.И.		12.03.26			

Копировал

Формат А0

Перв. примен.

Справ. №

Подп. и дата

Инв. № подл.

Взам. инв. №

Инв. № дубл.

Подп. и дата

Монтаж гидрооборудования на стенде

Формат	Зона	Поз.	Обозначение	Наименование	Кол.	Приме-чание
				Документация		
А0			ЛИМЦ.60148.13.000.000СБ	Сборочный чертеж		
				Сборочные единицы		
А4		1	ЛИМЦ.60148.13.001.000	Трубный зажим 18 двойной	10	
А4		2	ЛИМЦ.60148.13.002.000	Кран гидравлический	1	
А4		3	ЛИМЦ.60148.13.003.000	Трубопровод стояка	8	
А4		4	ЛИМЦ.60148.13.004.000	Трубопровод стояка	2	
А4		5	ЛИМЦ.60148.13.005.000	Трубопровод плеча внутреннего	4	
А4		6	ЛИМЦ.60148.13.006.000	Трубопровод плеча внешнего	2	
А4		7	ЛИМЦ.60148.13.006.000-01	Трубопровод плеча внешнего	2	
А4		8	ЛИМЦ.60148.13.007.000	Кронштейн	1	
А4		9	ЛИМЦ.60148.60.000.000	Шкаф гидравлический	1	
				Детали		
А3		10	ЛИМЦ.60148.13.000.001	Кронштейн	1	
А3		11	ЛИМЦ.60148.13.000.002	Кронштейн	1	
А3		12	ЛИМЦ.60148.13.000.003	Кронштейн	1	
		13	ЛИМЦ.60148.13.000.003-01	Кронштейн	1	
А3		14	ЛИМЦ.60148.13.000.004	Кронштейн	1	
		15	ЛИМЦ.60148.13.000.004-01	Кронштейн	1	
А4		16	ЛИМЦ.60148.13.000.005	Кронштейн	1	
А4		17	ЛИМЦ.60148.13.000.006	Кронштейн	1	

Перв. примен.

Справ. №

Подп. и дата

Инв. № дубл.

Взам. инв. №

Подп. и дата

Инв. № подл.

Изм.	Лист	№ докум.	Подп.	Дата
Разраб.		Нагуманов Н.Д.		12.03.26
Пров.		Макаров Е.В.		12.03.26
Н. контр.		Ванина А.Н.		12.03.26
Утв.		Сибирев М.И.		12.03.26

ЛИМЦ.60148.13.000.000

Монтаж гидрооборудования на стендере

Лит.	Лист	Листов
	1	5

АО "БТ"

Файл: ЛИМЦ.60148.13.000.000_Монтаж гидрооборудования на стендере

Шифр:

Копировал

Формат А4

Формат	Зона	Поз.	Обозначение	Наименование	Кол.	Приме-чание
А4		18	ЛИМЦ.60148.13.000.007	Футорка М42х2–М22х1,5	2	
А4		19	ЛИМЦ.60148.13.000.008	Футорка М42х2–М16х1,5	2	
А4		20	ЛИМЦ.60148.13.000.009	Футорка М27х1,5–М16х1,5	2	
А4		21	ЛИМЦ.60148.13.000.010	Футорка М20х1,5–М16х1,5	2	
				Стандартные изделия		
		22		Винт с цилиндрической головкой и шестигранным углублением под ключ ГОСТ Р ИСО 4762 – М6х25 – А2–70	74	
		23		Винт с шестигранной головкой ГОСТ Р ИСО 4017 – М8х20 – А2–70	8	
		24		Винт с шестигранной головкой ГОСТ Р ИСО 4017 – М10х30 – А2–70	28	
		25		Винт с цилиндрической головкой и шестигранным углублением под ключ ГОСТ Р ИСО 4762 – М12х20 – А2–70	4	
		26		Гайка шестигранная нормальная ГОСТ ISO 4032 – М6 – А2–70	152	
		27		Гайка шестигранная нормальная ГОСТ ISO 4032 – М8 – А2–70	8	
		28		Гайка шестигранная нормальная ГОСТ ISO 4032 – М10 – А2–70	28	

Подп. и дата | Инв. № дубл. | Взам. инв. № | Подп. и дата | Инв. № подл.

Изм.	Лист	№ докум.	Подп.	Дата	ЛИМЦ.60148.13.000.000	Лист 2

Шифр: Копировал Формат А4

Файл: ЛИМЦ.60148.13.000.000_Монтаж гидрооборудования на стенде

Формат	Зона	Поз.	Обозначение	Наименование	Кол.	Приме-чание
		29		Шайба 10 3Х13 ГОСТ 6402-70	12	
		30		Шайба А.6.21 ГОСТ 11371-78	78	
		31		Шайба А.8.21 ГОСТ 11371-78	12	
		32		Шайба А.10.02.0221 ГОСТ 11371-78	32	
		33		Шайба А.10.21 ГОСТ 11371-78	24	
				Прочие изделия		
		34		Гайка ADES M6 (AEGI)	188	
		35		Планка ABINS-2 L=201 (AEGI)	10	
		36		Планка ABINS-2 L=90 (AEGI)	22	
		37		Муфта разрывная	2	
				LPGPN34SN		
		38		РВД DN 16 DKO-L (Г) 26х1.5	2	
				18 Нерж/2SN DN 16 P=165		
				L=2000/DN 16 DKO-L (Г)		
				26х1.5 18 Нерж		
		39		РВД DN 10 DKO-L (Г) 18х1.5 12	13	
				Нерж/2SN DN 10 P=330		
				L=2000/DN 10 DKO-L (Г)		
				18х1.5 12 Нерж		
		40		РВД DN 16 DKO-L (Г) 26х1.5	2	
				18 (90) Нерж/2SN DN 16		
				P=165 L=3000/DN 16 DKO-L		
				(Г) 26х1.5 18 (90) Нерж		
		41		РВД DN 10 DKO-L (Г) 18х1.5 12	2	
				(90) Нерж/2SN DN 10 P=330		
				L=1500/DN 10 DKO-L (Г)		
				18х1.5 12 (90) Нерж		

Подп. и дата | Инв. № дубл. | Взам. инв. № | Подп. и дата | Инв. № подл.

Изм.	Лист	№ докум.	Подп.	Дата	ЛИМЦ.60148.13.000.000	Лист 3

Шифр: Копировал Формат А4

Файл: ЛИМЦ.60148.13.000.000_Монтаж гидрооборудования на стенде

Формат	Зона	Поз.	Обозначение	Наименование	Кол.	Приме-чание
		42		РВД DN 10 DKO-L (Г) 18x1.5 12	2	
				(90) Нерж/2SN DN 10 P=330		
				L=4000/DN 10 DKO-L (Г)		
				18x1.5 12 (90) Нерж		
		43		РВД DN 10 DKO-L (Г) 18x1.5 12	1	
				(90) Нерж/2SN DN 10 P=330		
				L=3000/DN 10 DKO-L (Г)		
				18x1.5 12 (90) Нерж		
		44		РВД DN 10 DKO-L (Г) 18x1.5 12	6	
				Нерж/2SN DN 10 P=330		
				L=2500/DN 10 DKO-L (Г)		
				18x1.5 12 Нерж		
		45		РВД DN 10 DKO-L (Г) 18x1.5 12	1	
				Нерж/2SN DN 10 P=330		
				L=3000/DN 10 DKO-L (Г)		
				18x1.5 12 (90) Нерж		
		46		РВД DN 10 DKO-L (Г) 18x1.5 12	1	
				Нерж/2SN DN 10 P=330		
				L=2000/DN 10 DKO-L (Г)		
				18x1.5 12 (90) Нерж		
		47		РВД DN 10 DKO-L (Г) 18x1.5 12	2	
				Нерж / 2SN DN 10 P=330		
				L=1500 / DN 10 DKO-L (Г)		
				18x1.5 12 (90) Нерж		
		48		Трубный зажим Ф12 double	84	
				(AEGI)		
		49		Трубный зажим Ф18 single	2	
				(AEGI)		
		–		Трубный зажим D18, double	10	
				(AEGI) (Заготовка для		
				ЛИМЦ.60148.13.001.000)		

Подп. и дата | Инв. № дубл. | Взам. инв. № | Подп. и дата | Инв. № подл.

Изм.	Лист	№ докум.	Подп.	Дата	ЛИМЦ.60148.13.000.000	Лист 4

Шифр: Копировал Формат А4

Файл: ЛИМЦ.60148.13.000.000_Монтаж гидрооборудования на стенде

Формат	Зона	Поз.	Обозначение	Наименование	Кол.	Приме-чание
		50		Штуцер прямой GEV-12LNPT	4	
				3/4		
		51		Штуцер прямой дюймовый	2	
				BSP (уплотнение B) Код		
				110332.1 (CAST)		
		52		Штуцер прямой метрический,	6	
				уплотнение B Код 110407.1		
				(CAST)		
		53		Штуцер прямой метрический,	2	
				уплотнение B Код 110409.1		
				(CAST)		

Подп. и дата | Инв. № дубл. | Взам. инв. № | Подп. и дата | Инв. № подл.

Изм.	Лист	№ докум.	Подп.	Дата	ЛИМЦ.60148.13.000.000	Лист 5

Шифр: Копировал Формат А4

Файл: ЛИМЦ.60148.13.000.000_Монтаж гидрооборудования на стенде